
The Black Box


Portland, Oregon

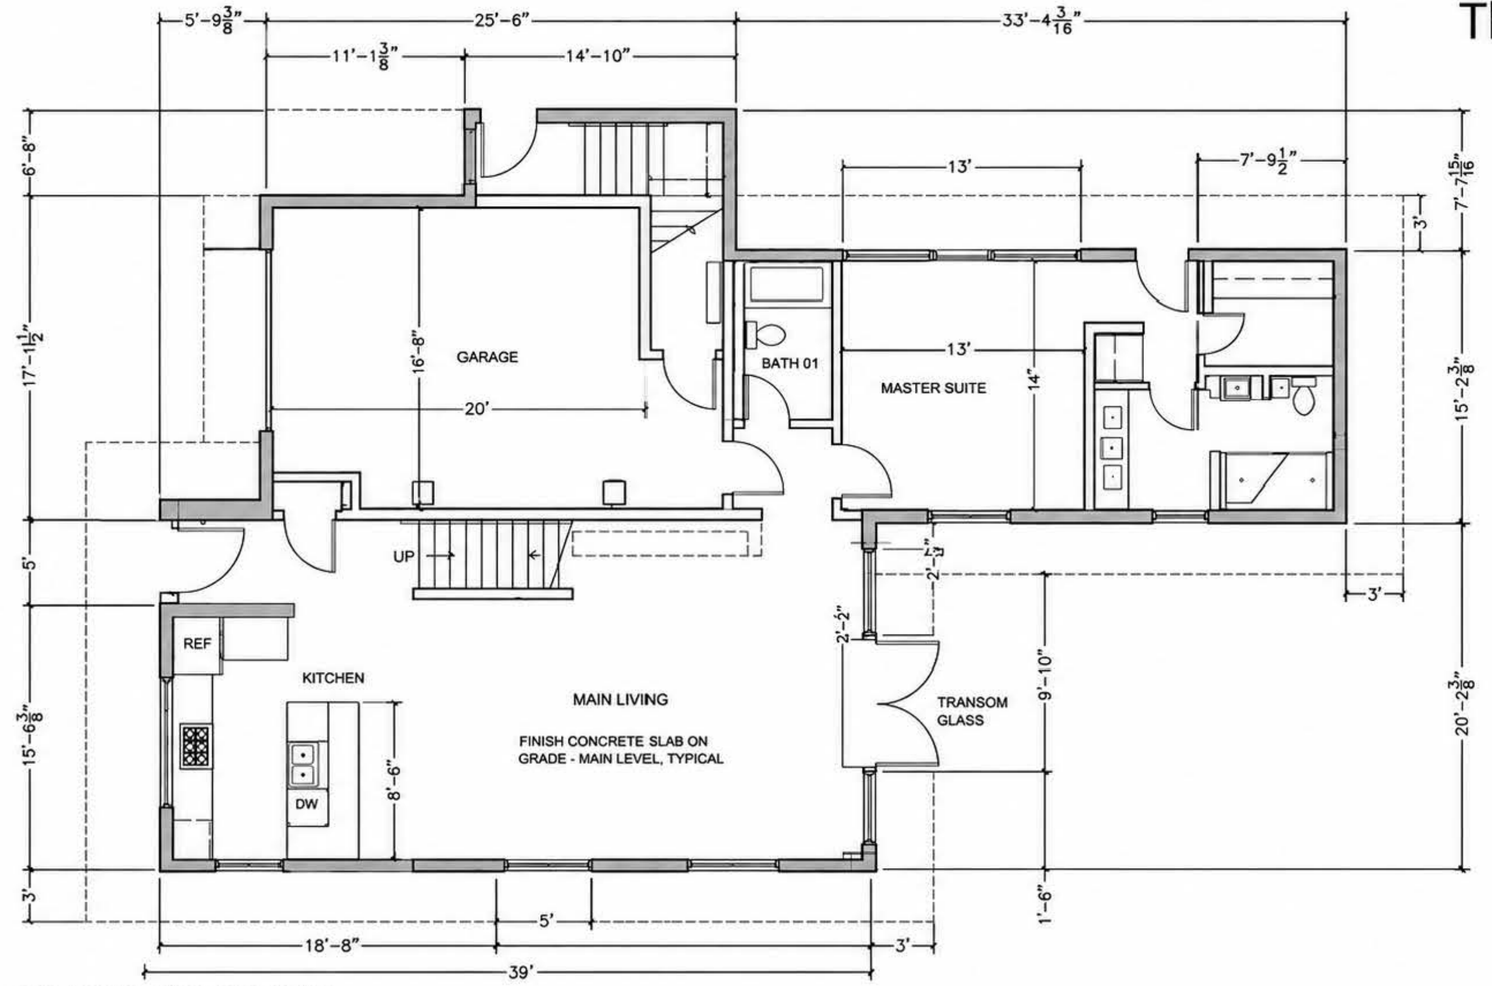

1 FIRST FLOOR PLAN

The Black Box


Portland, Oregon

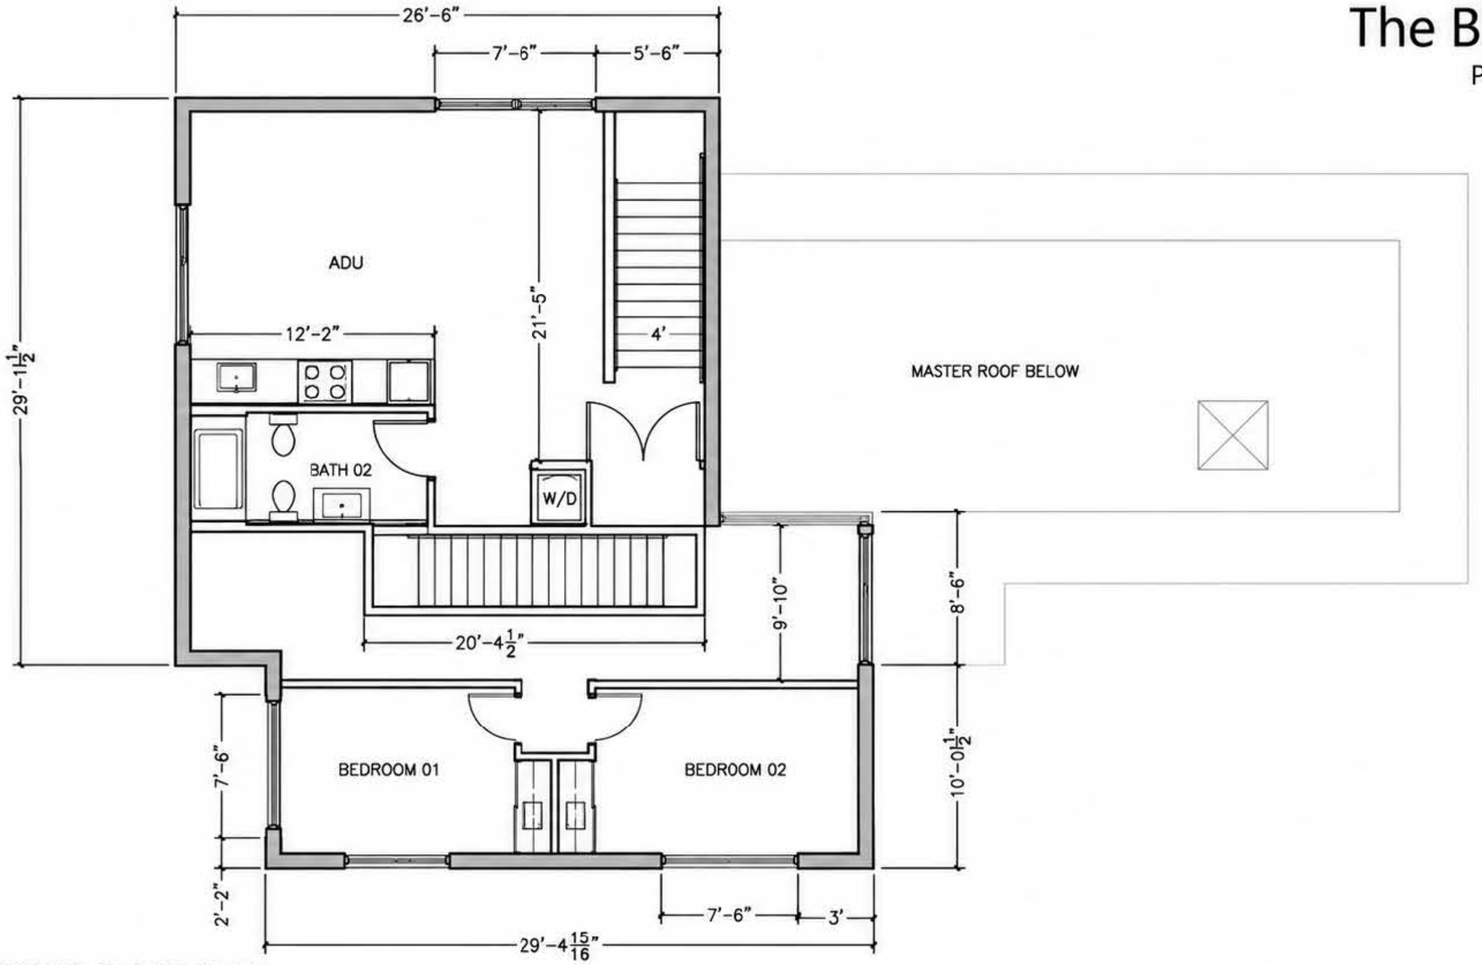

1 SECOND FLOOR PLAN

The Black Box

Portland, Oregon

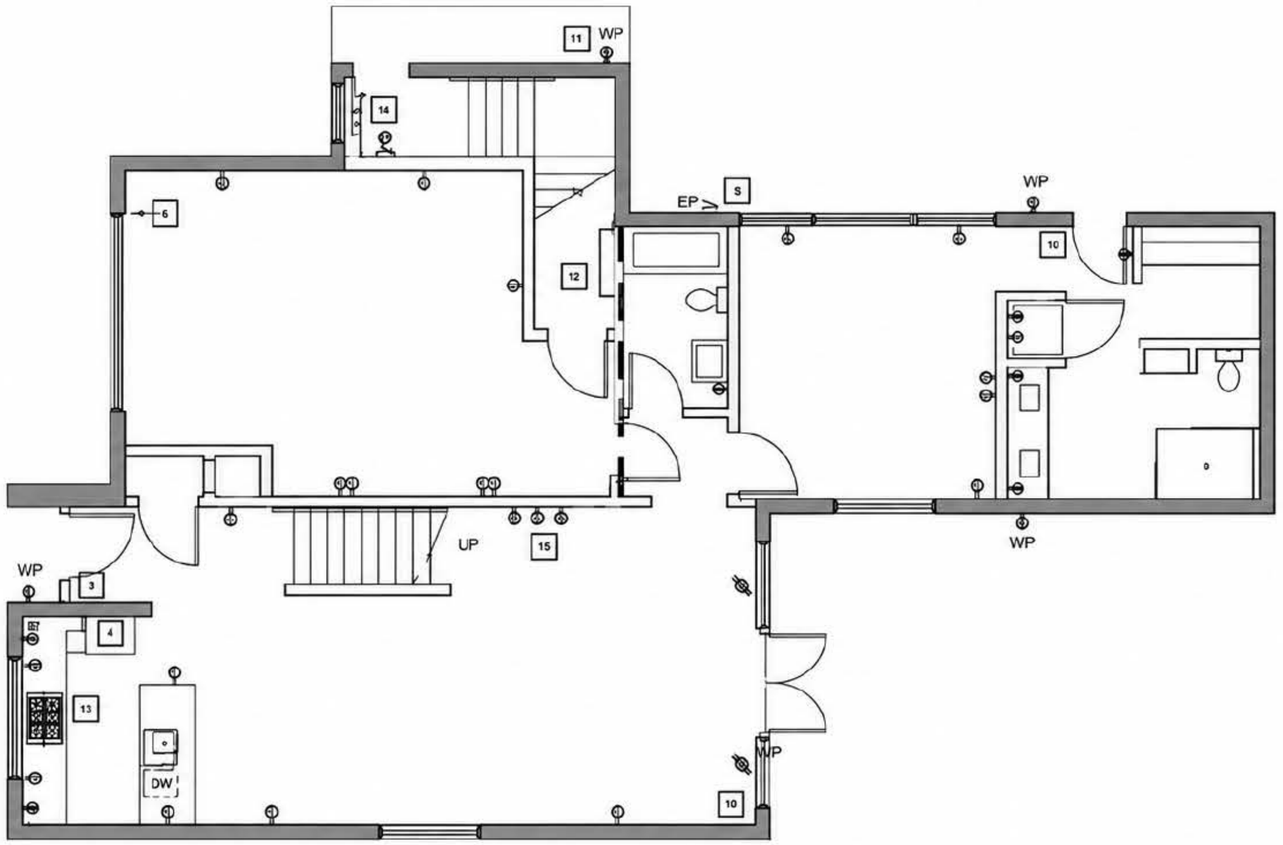


ELECTRICAL LEGEND

- DUPLEX
- FOURPLEX
- DEDICATED 208 - 240 VOLT
- GFCI
- S — SWITCH
- EP — ELECTRICAL PANEL
- WP — WEATHERPROOF OUTLET

1 MAIN FLOOR POWER PLAN

The Black Box

Portland, Oregon

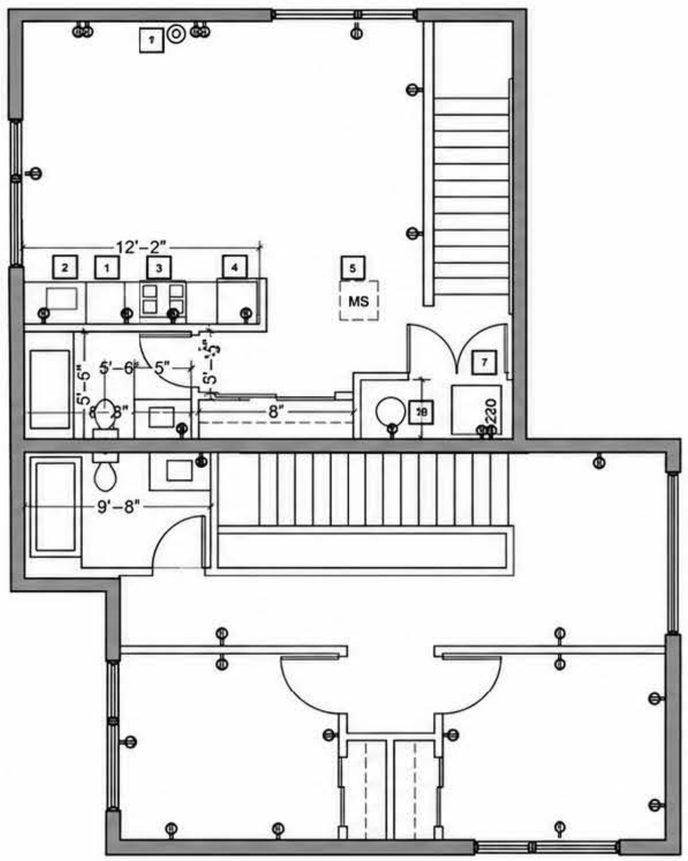


ELECTRICAL LEGEND

- DUPLEX
- FOURPLEX
- DEDICATED 208 - 240 VOLT
- GFCI
- S — SWITCH
- EP — ELECTRICAL PANEL
- WP — WEATHERPROOF OUTLET

1 UPPER FLOOR POWER PLAN

The Black Box

Portland, Oregon

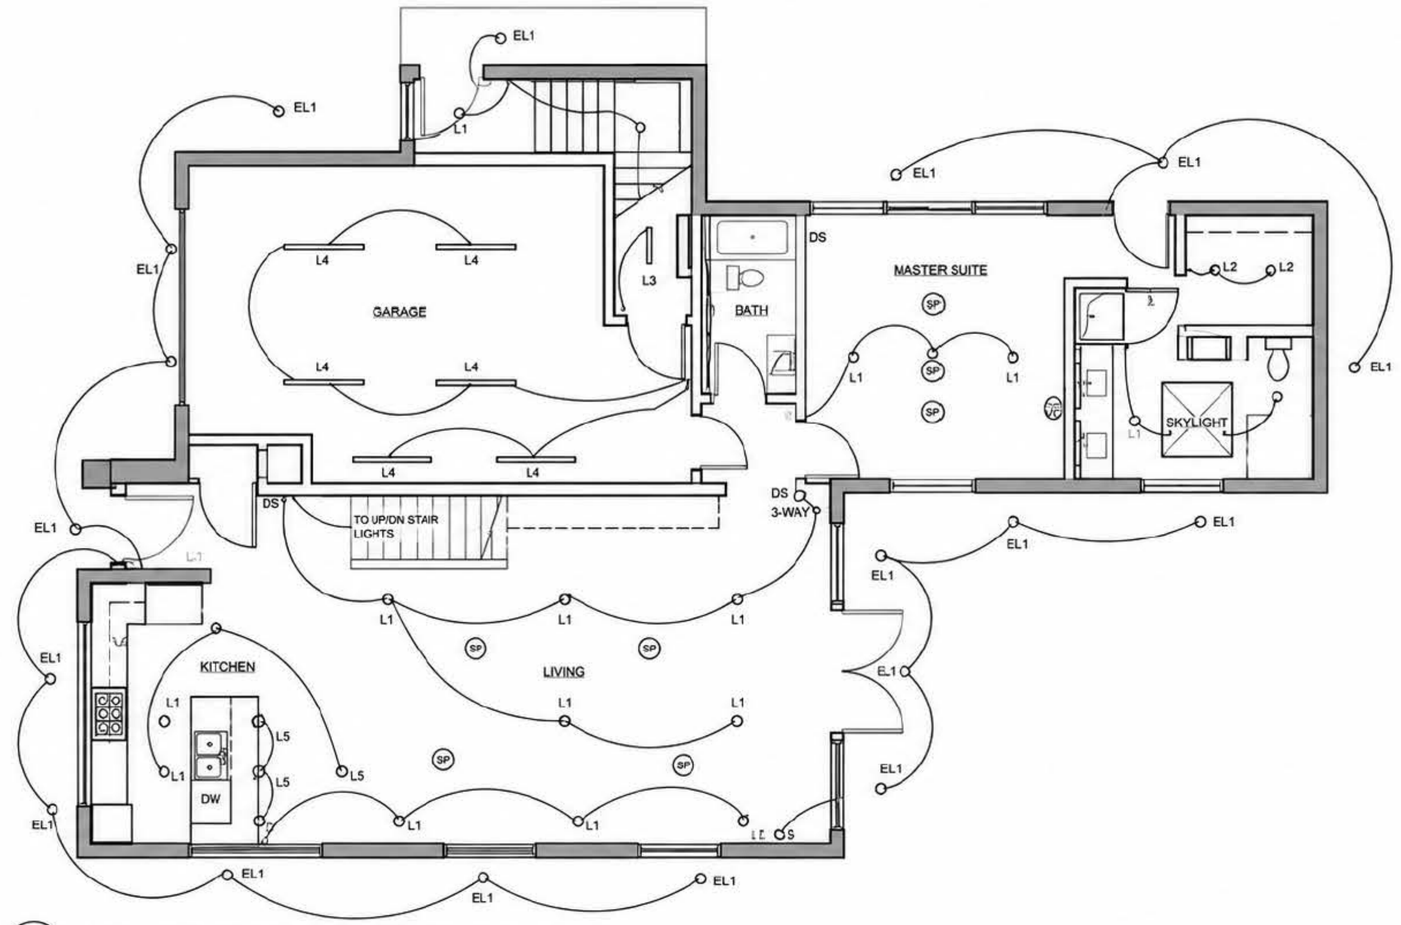


1 MAIN FLOOR REFLECTED CEILING PLAN

RCP LEGEND

	DIRECTIONAL DOWNLIGHT
	DOWNLIGHT
	DIRECTIONAL ACCENT LIGHT
	PENDANT LIGHT
J	J-BOX
	FLUORESCENT STRIP
	TASK LIGHT
S	SWITCH
DS	DIMMER SWITCH
3-WAY	THREE-WAY SWITCH
EL1	EXTERIOR LIGHT
SP	FLUSH MOUNTED CEILING SPEAKER
VC	VOLUME CONTROL FOR SPEAKER SYSTEM

The Black Box

Portland, Oregon

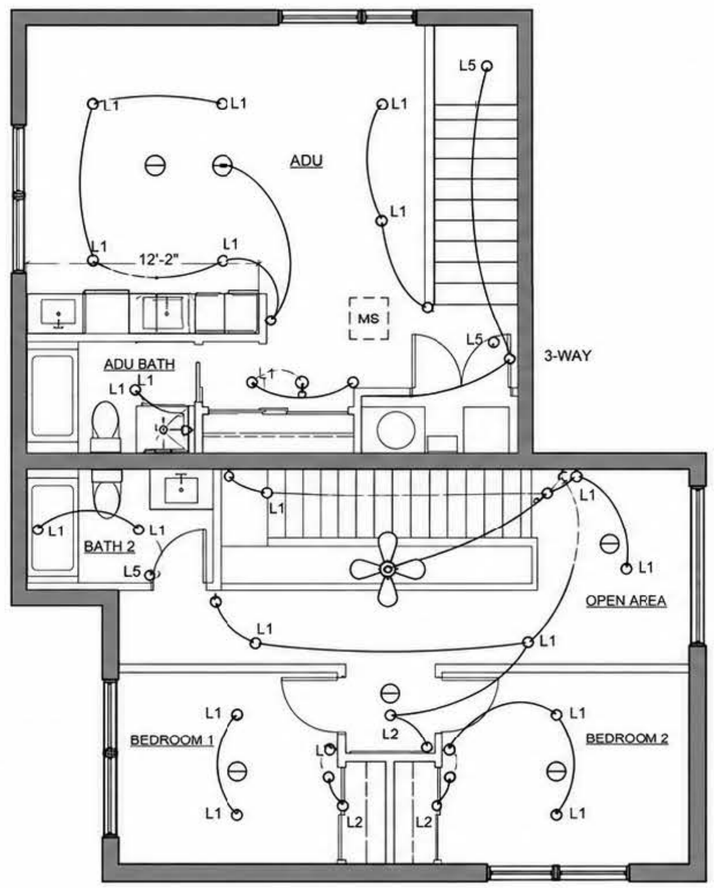

RCP LEGEND

	DIRECTIONAL DOWNLIGHT
	DOWNLIGHT
	DIRECTIONAL ACCENT LIGHT
	PENDANT LIGHT
J	J-BOX
	FLUORESCENT STRIP
	TASK LIGHT
S	SWITCH
DS	DIMMER SWITCH
3-WAY	THREE-WAY SWITCH
L1	EXTERIOR LIGHT
SP	FLUSH MOUNTED CEILING SPEAKER
VC	VOLUME CONTROL FOR SPEAKER SYSTEM


1 SECOND FLOOR REFLECTED CEILING PLAN

The Black Box

Portland, Oregon



1 WEST ELEVATION

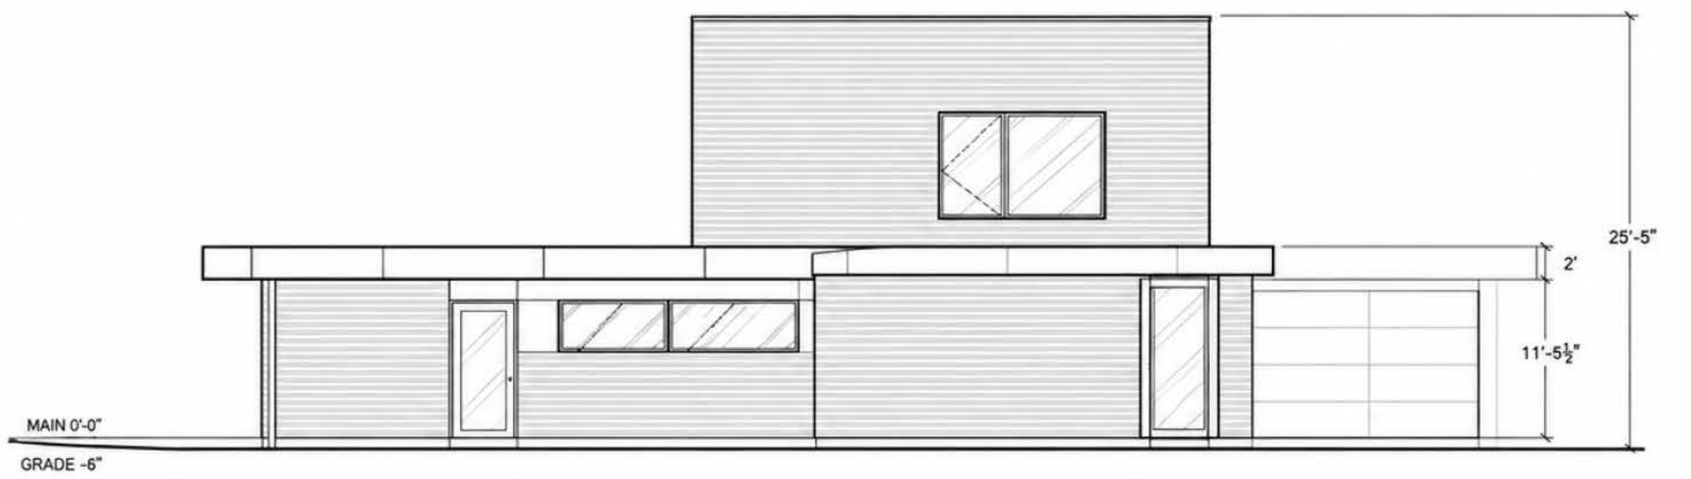


2 SOUTH ELEVATION

The Black Box

Portland, Oregon



1 EAST ELEVATION

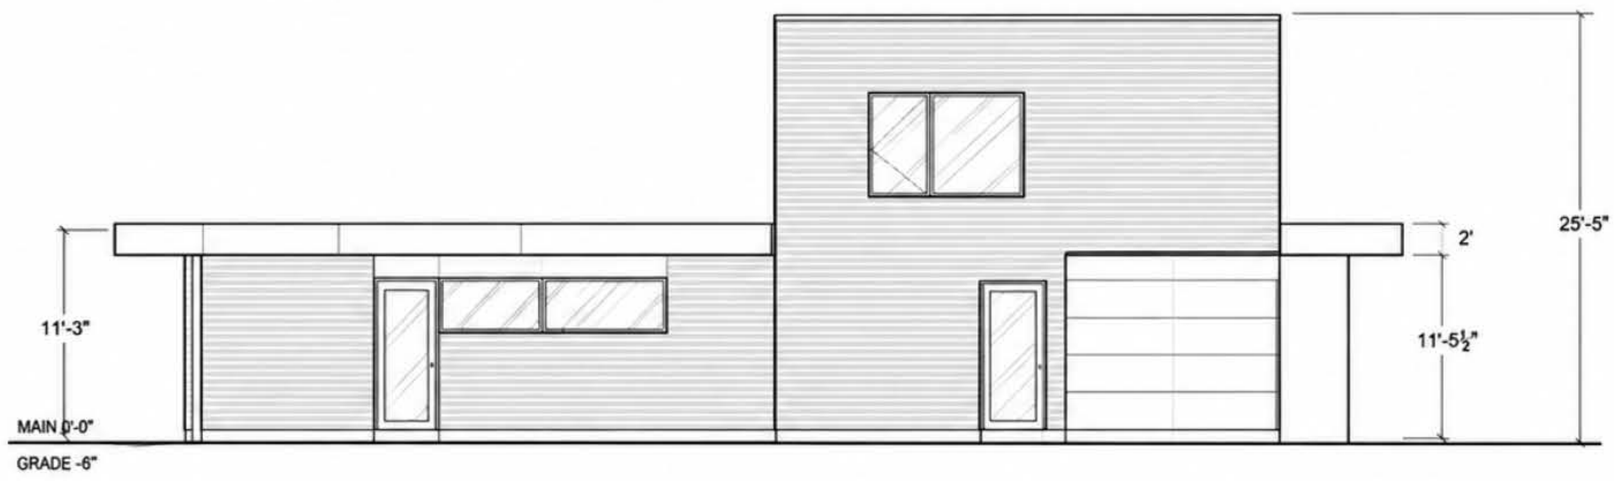

2 NORTH ELEVATION